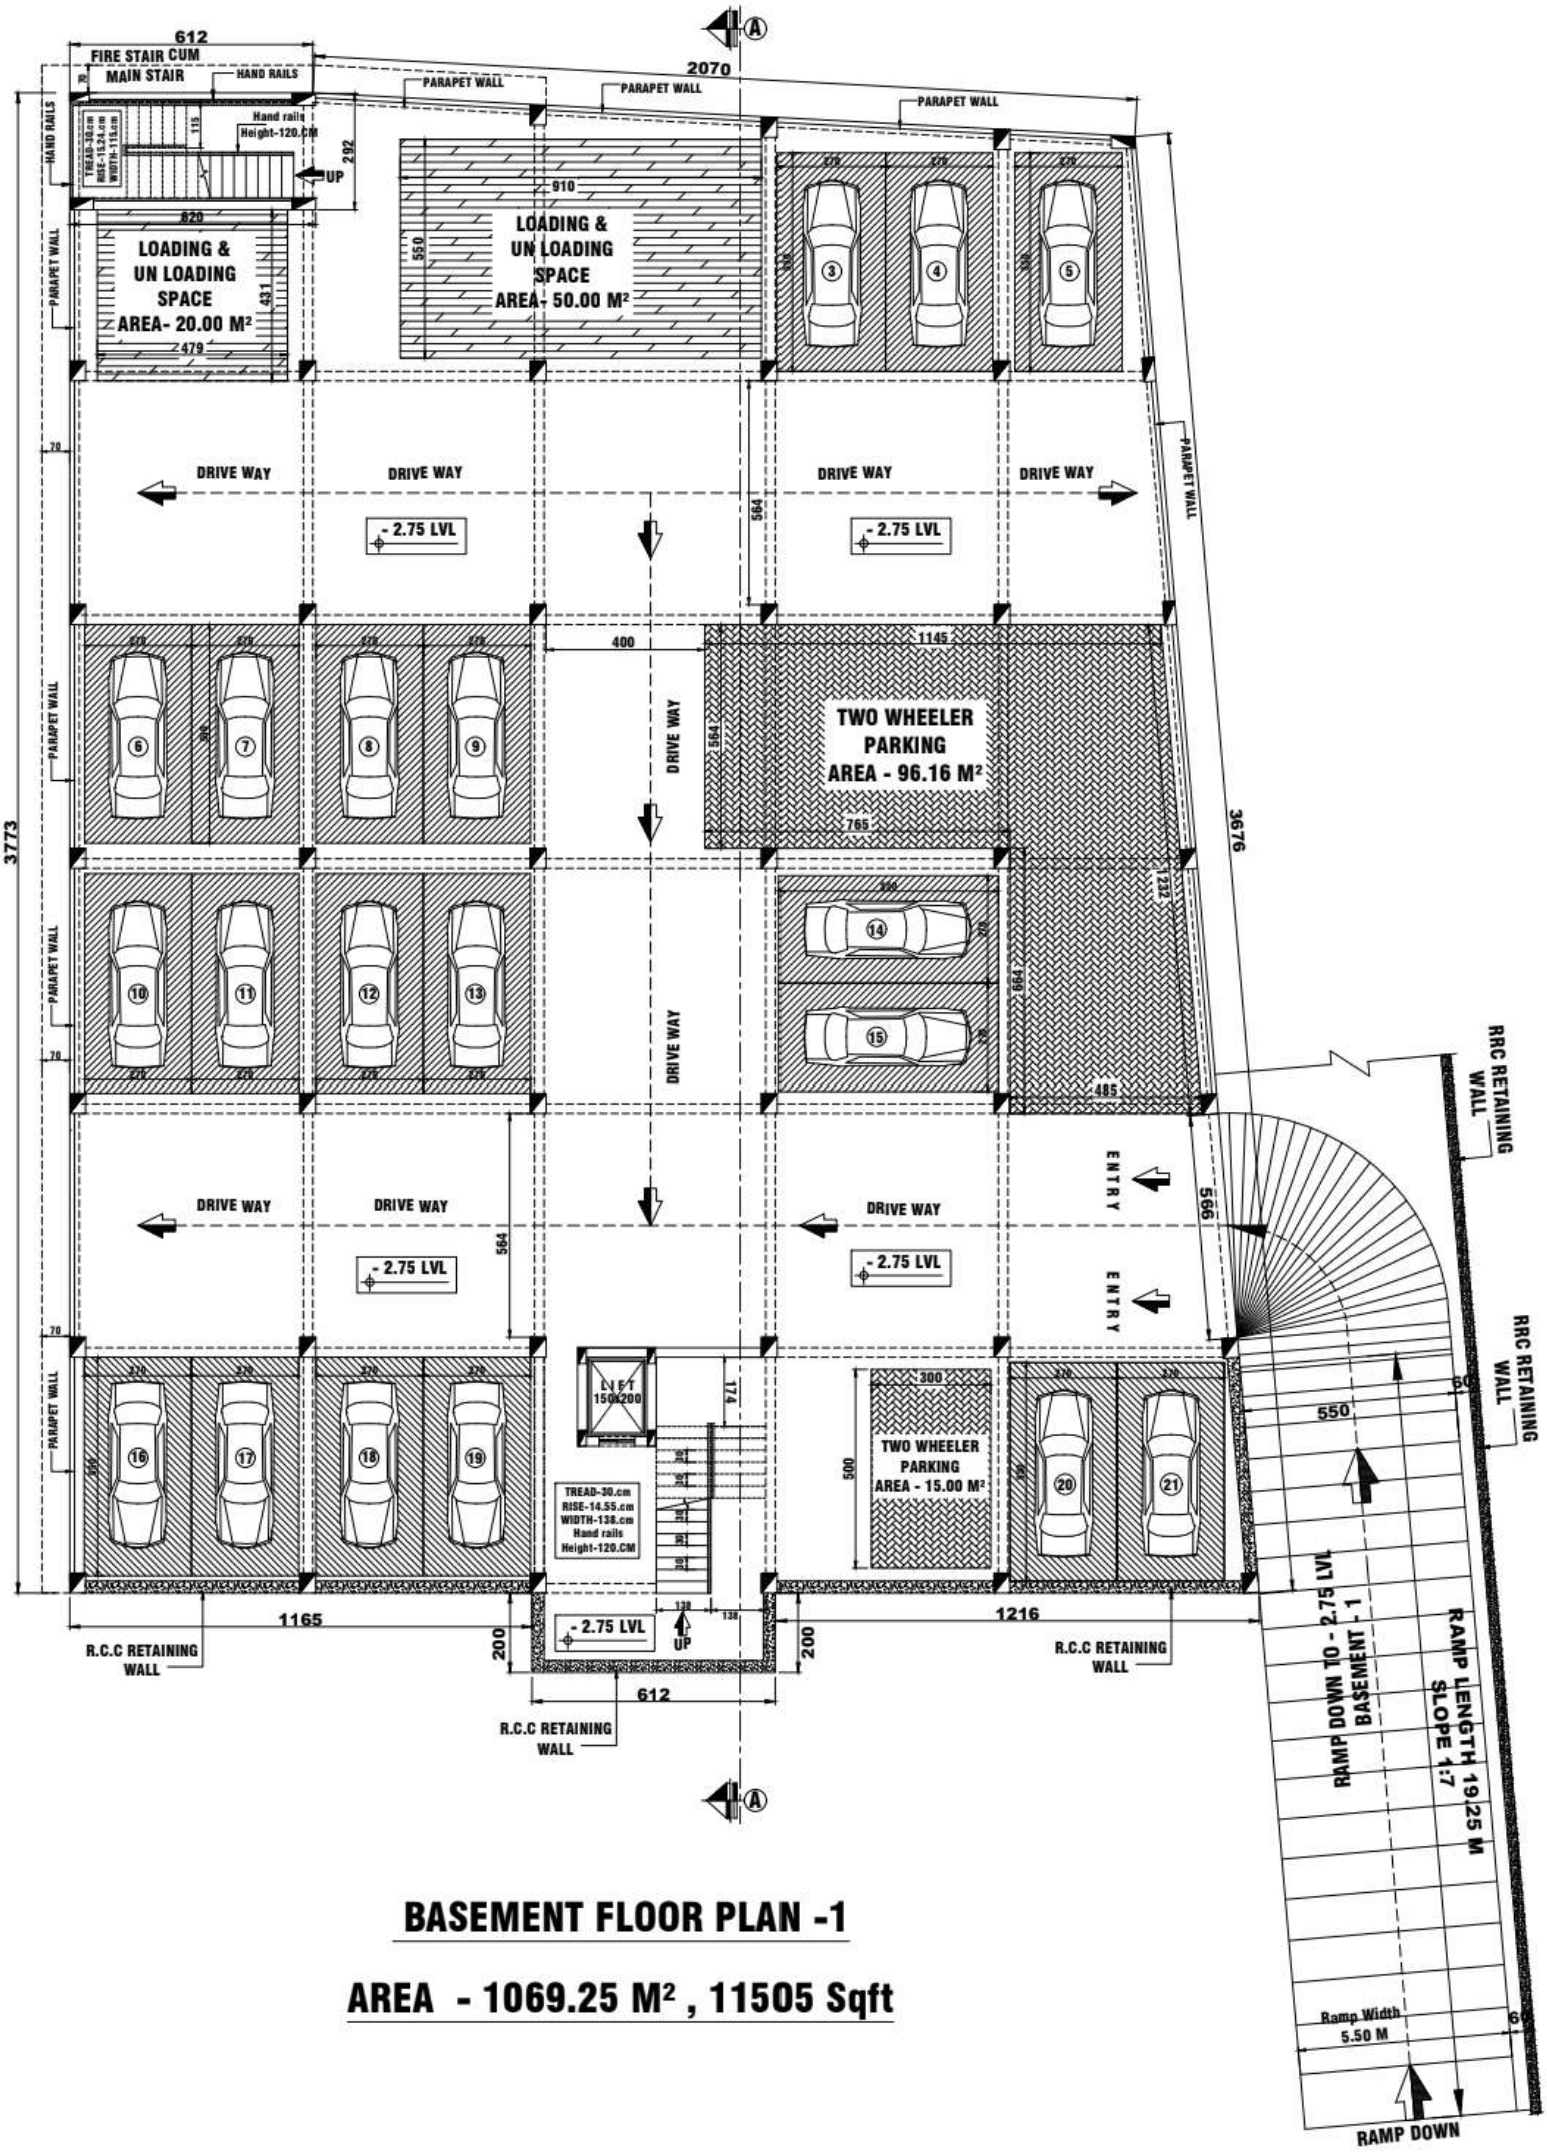

BASEMENT FLOOR PLAN -1

AREA - 1069.25 M², 11505 Sqft

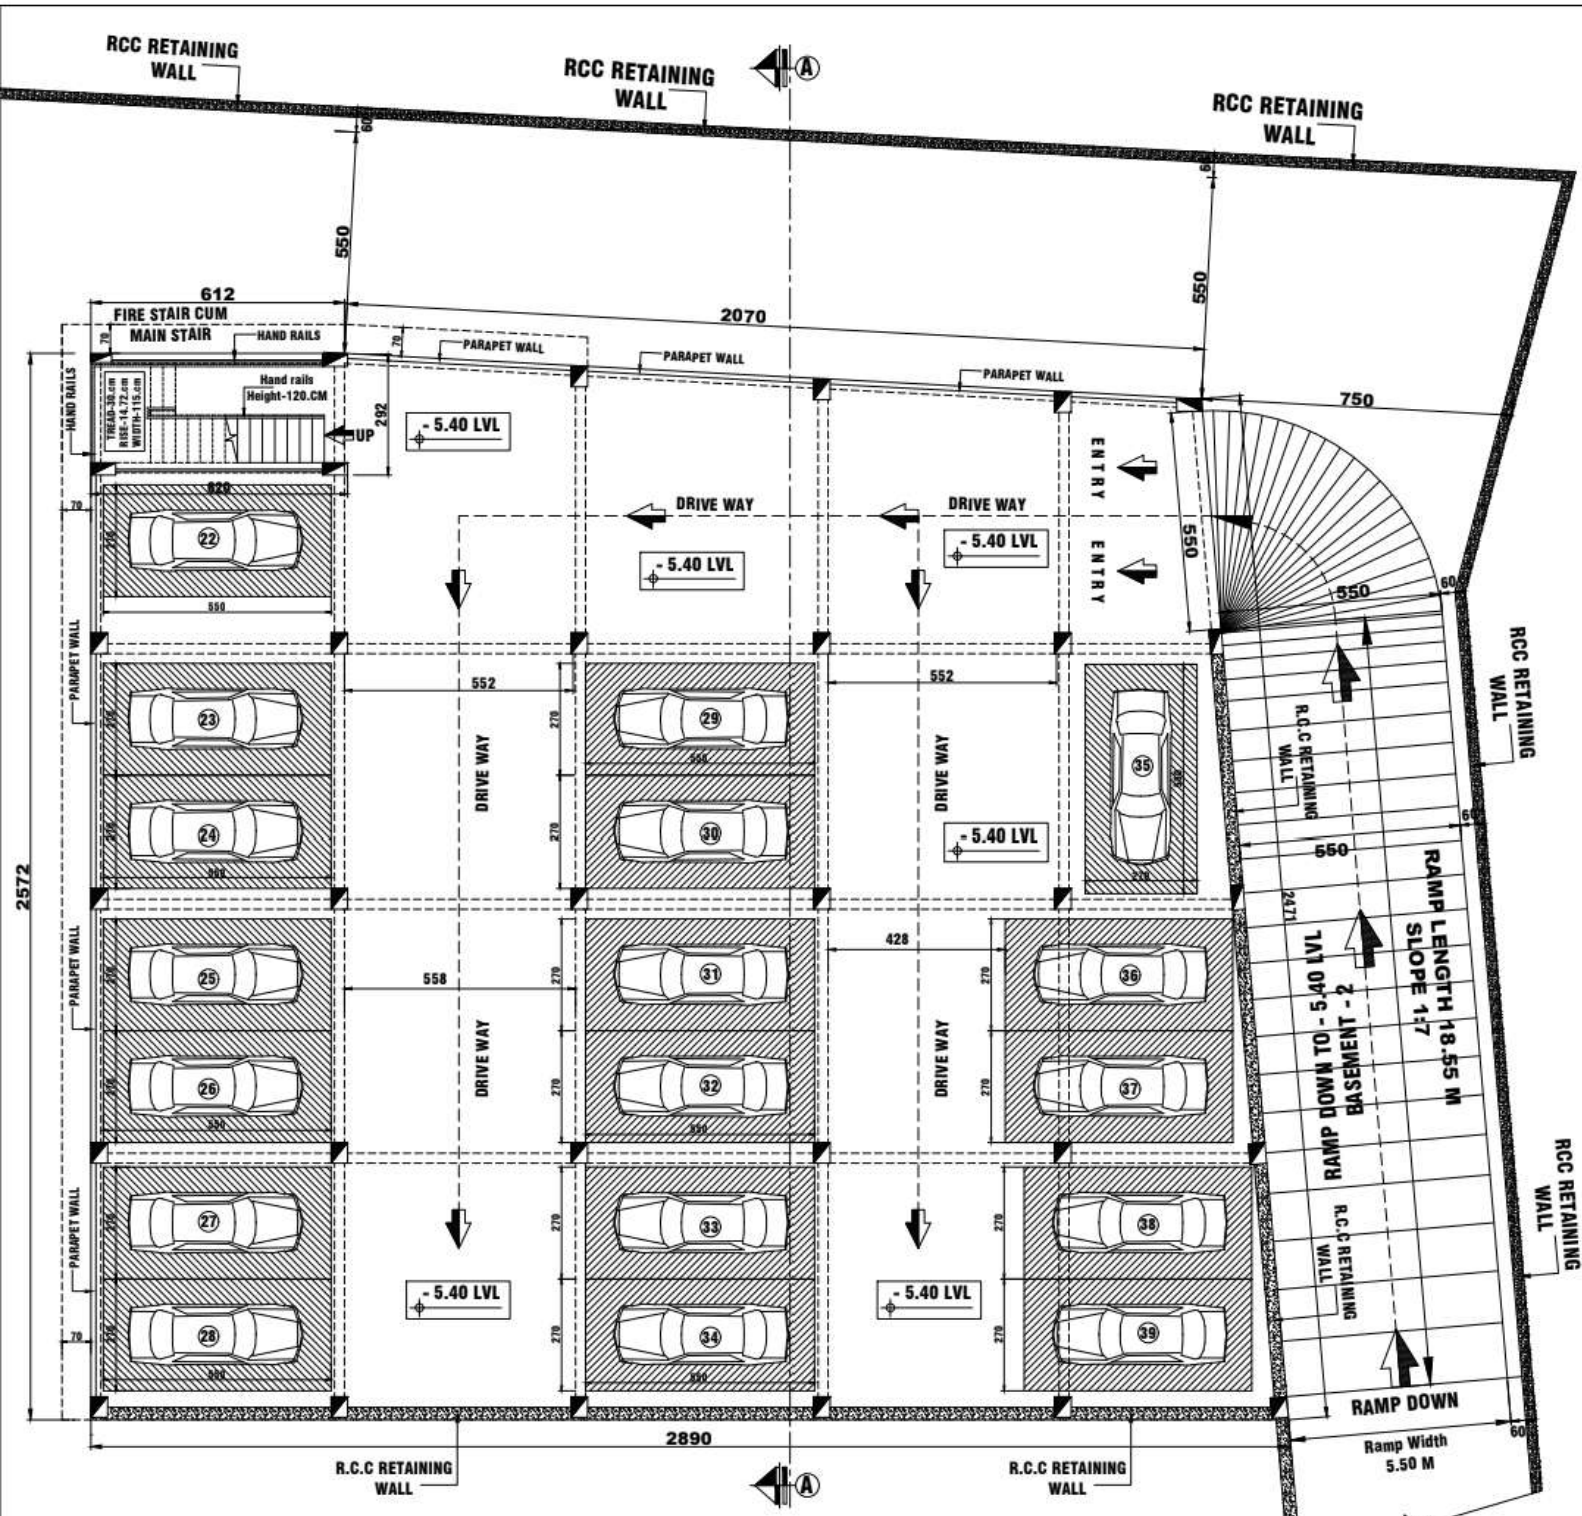

BASEMENT FLOOR PLAN -2

AREA - 703.70 M², 7572 Sqft

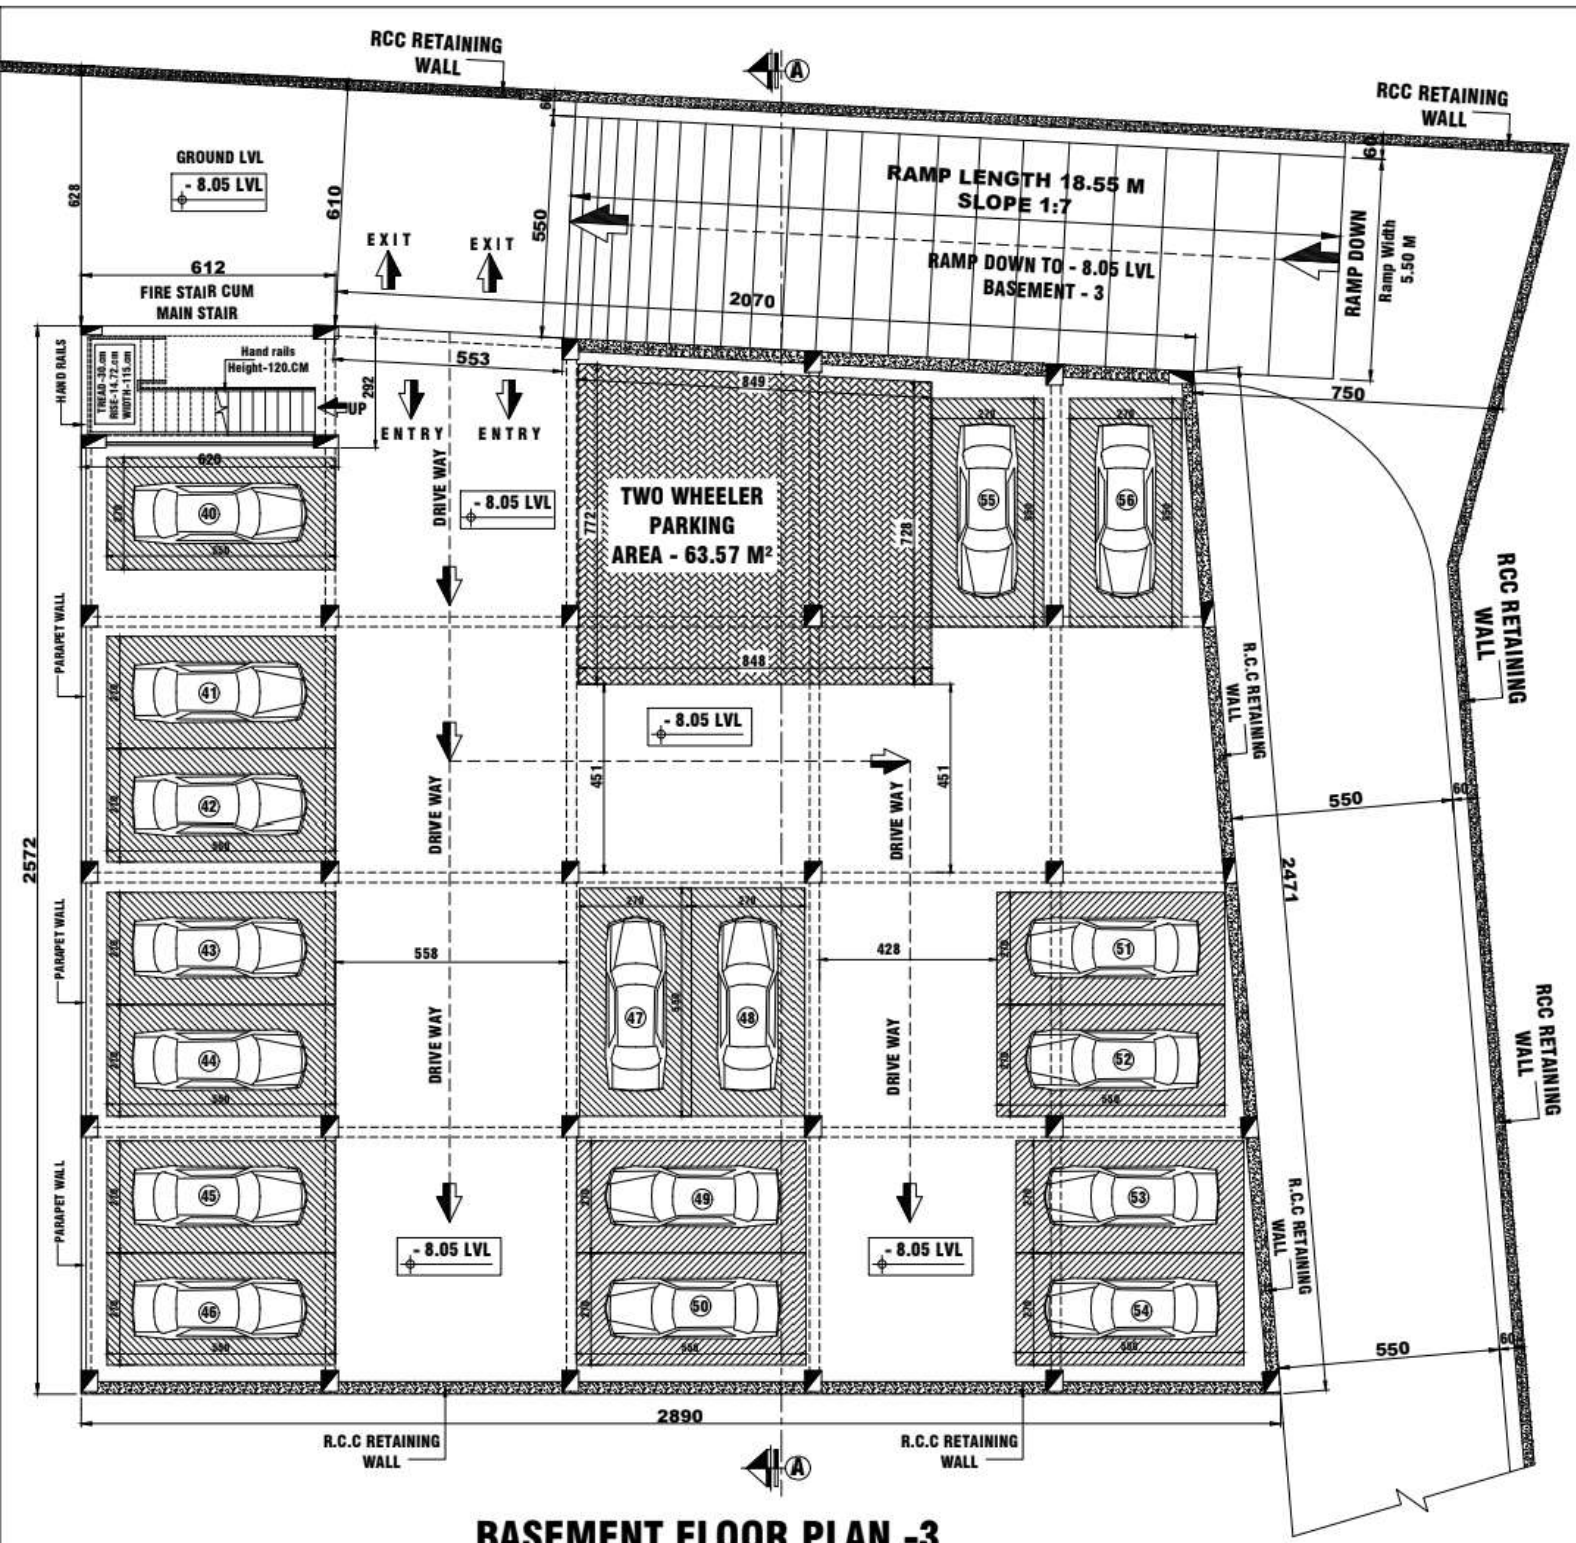

BASEMENT FLOOR PLAN -3

AREA - 703.70 M², 7572 Sqft

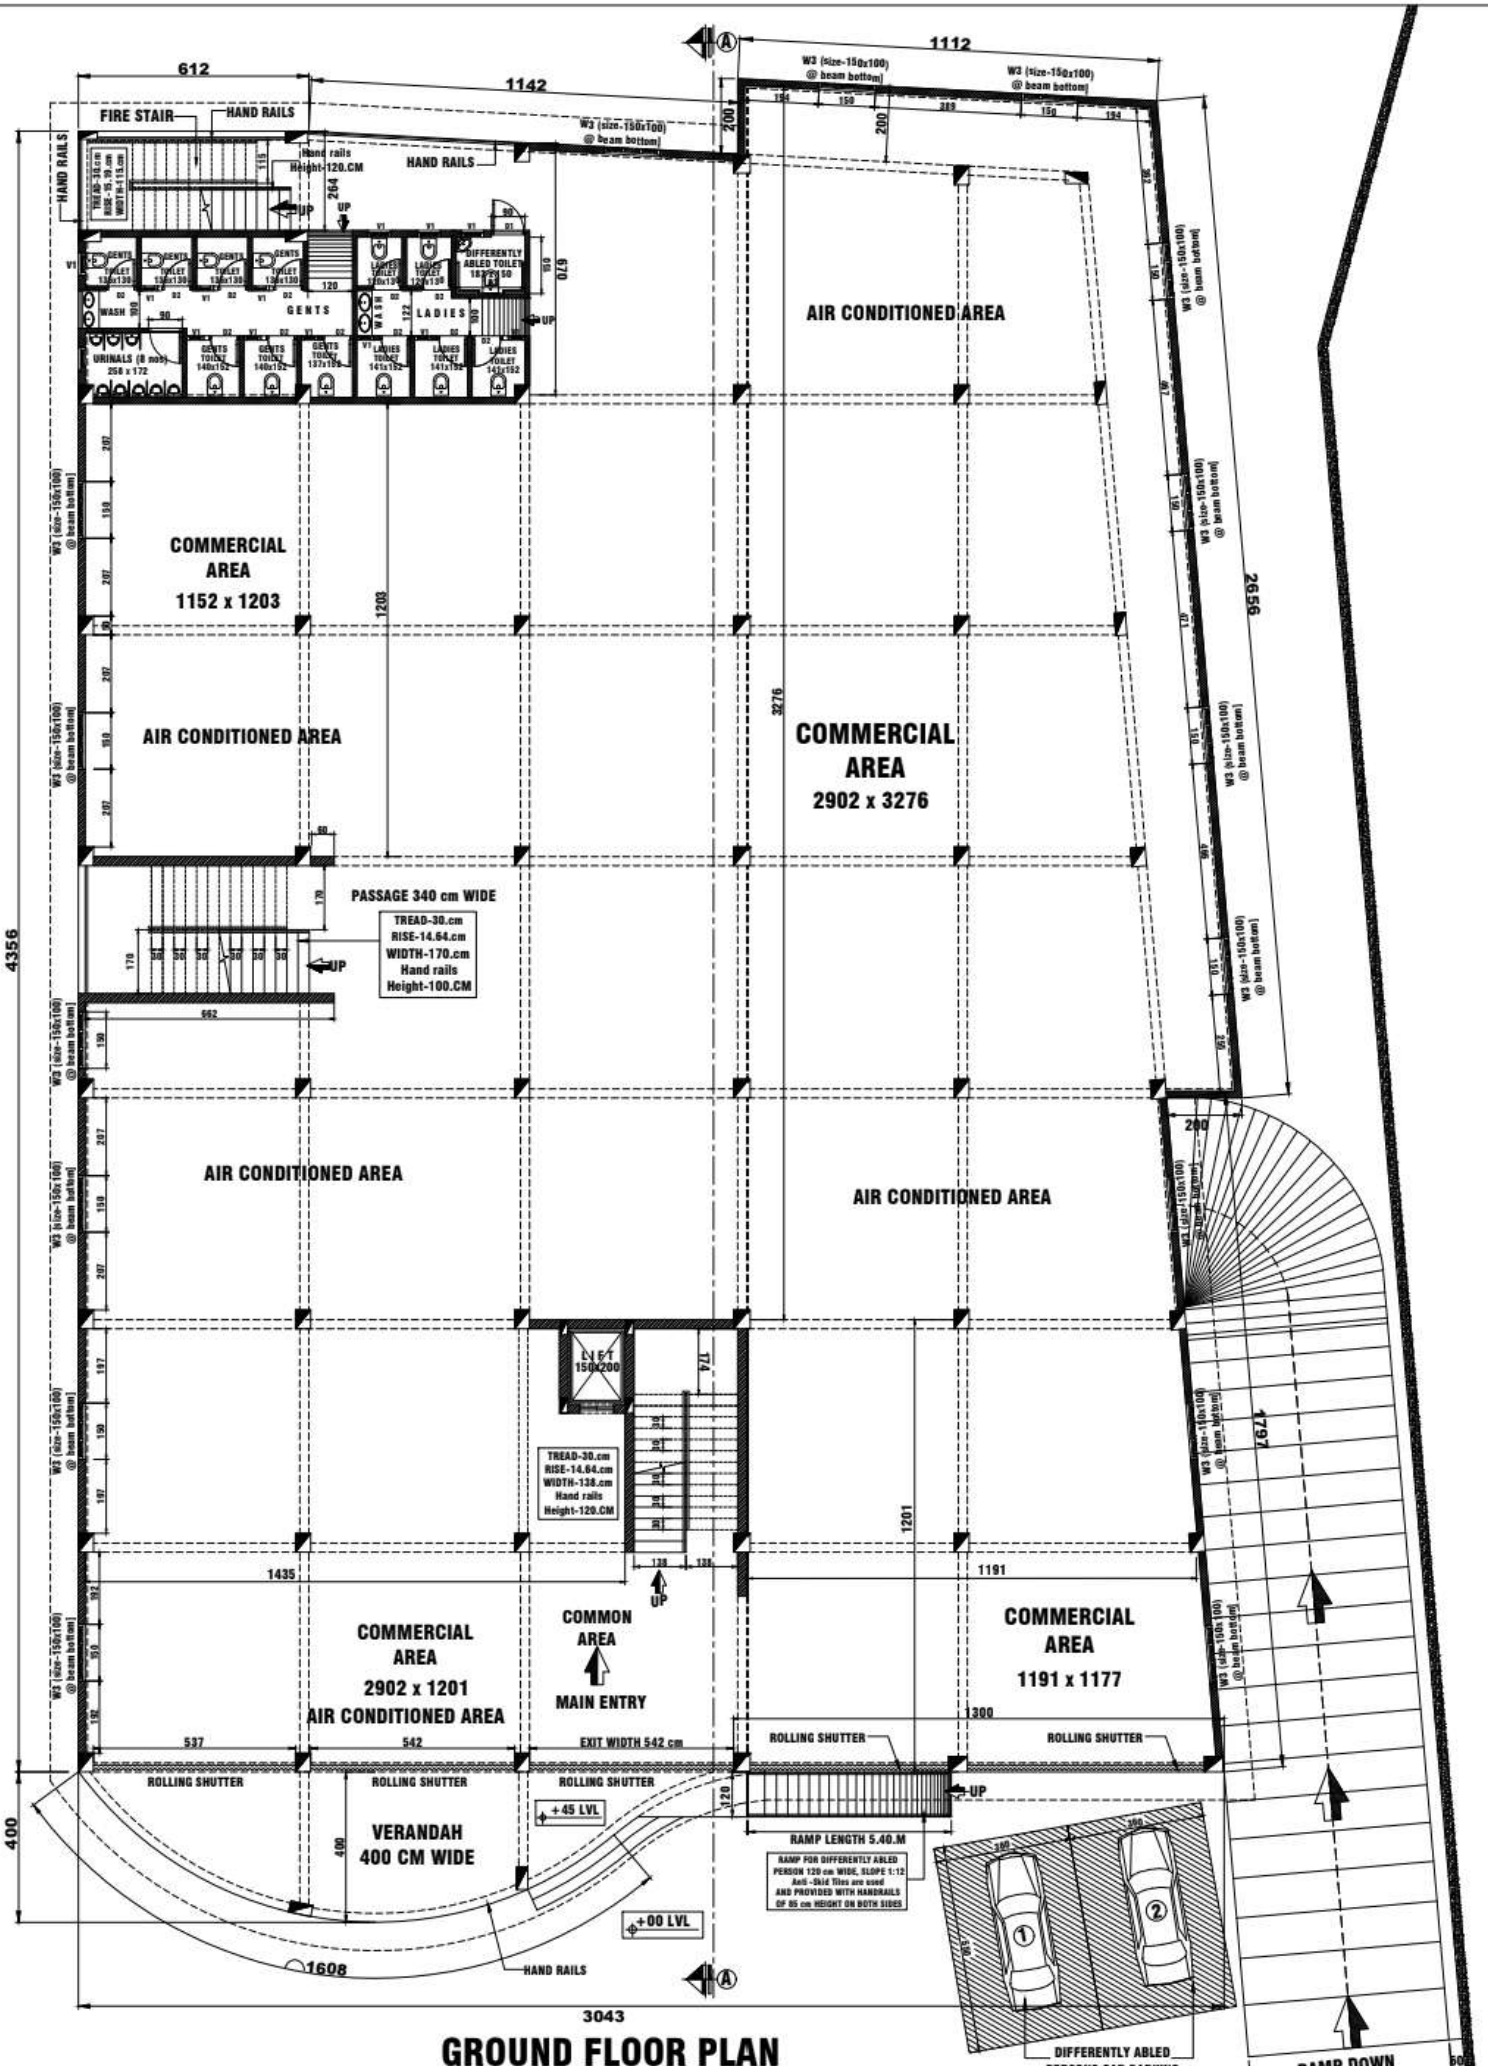

GROUND FLOOR PLAN

AREA - 1350.00 M², 14526 Sqft

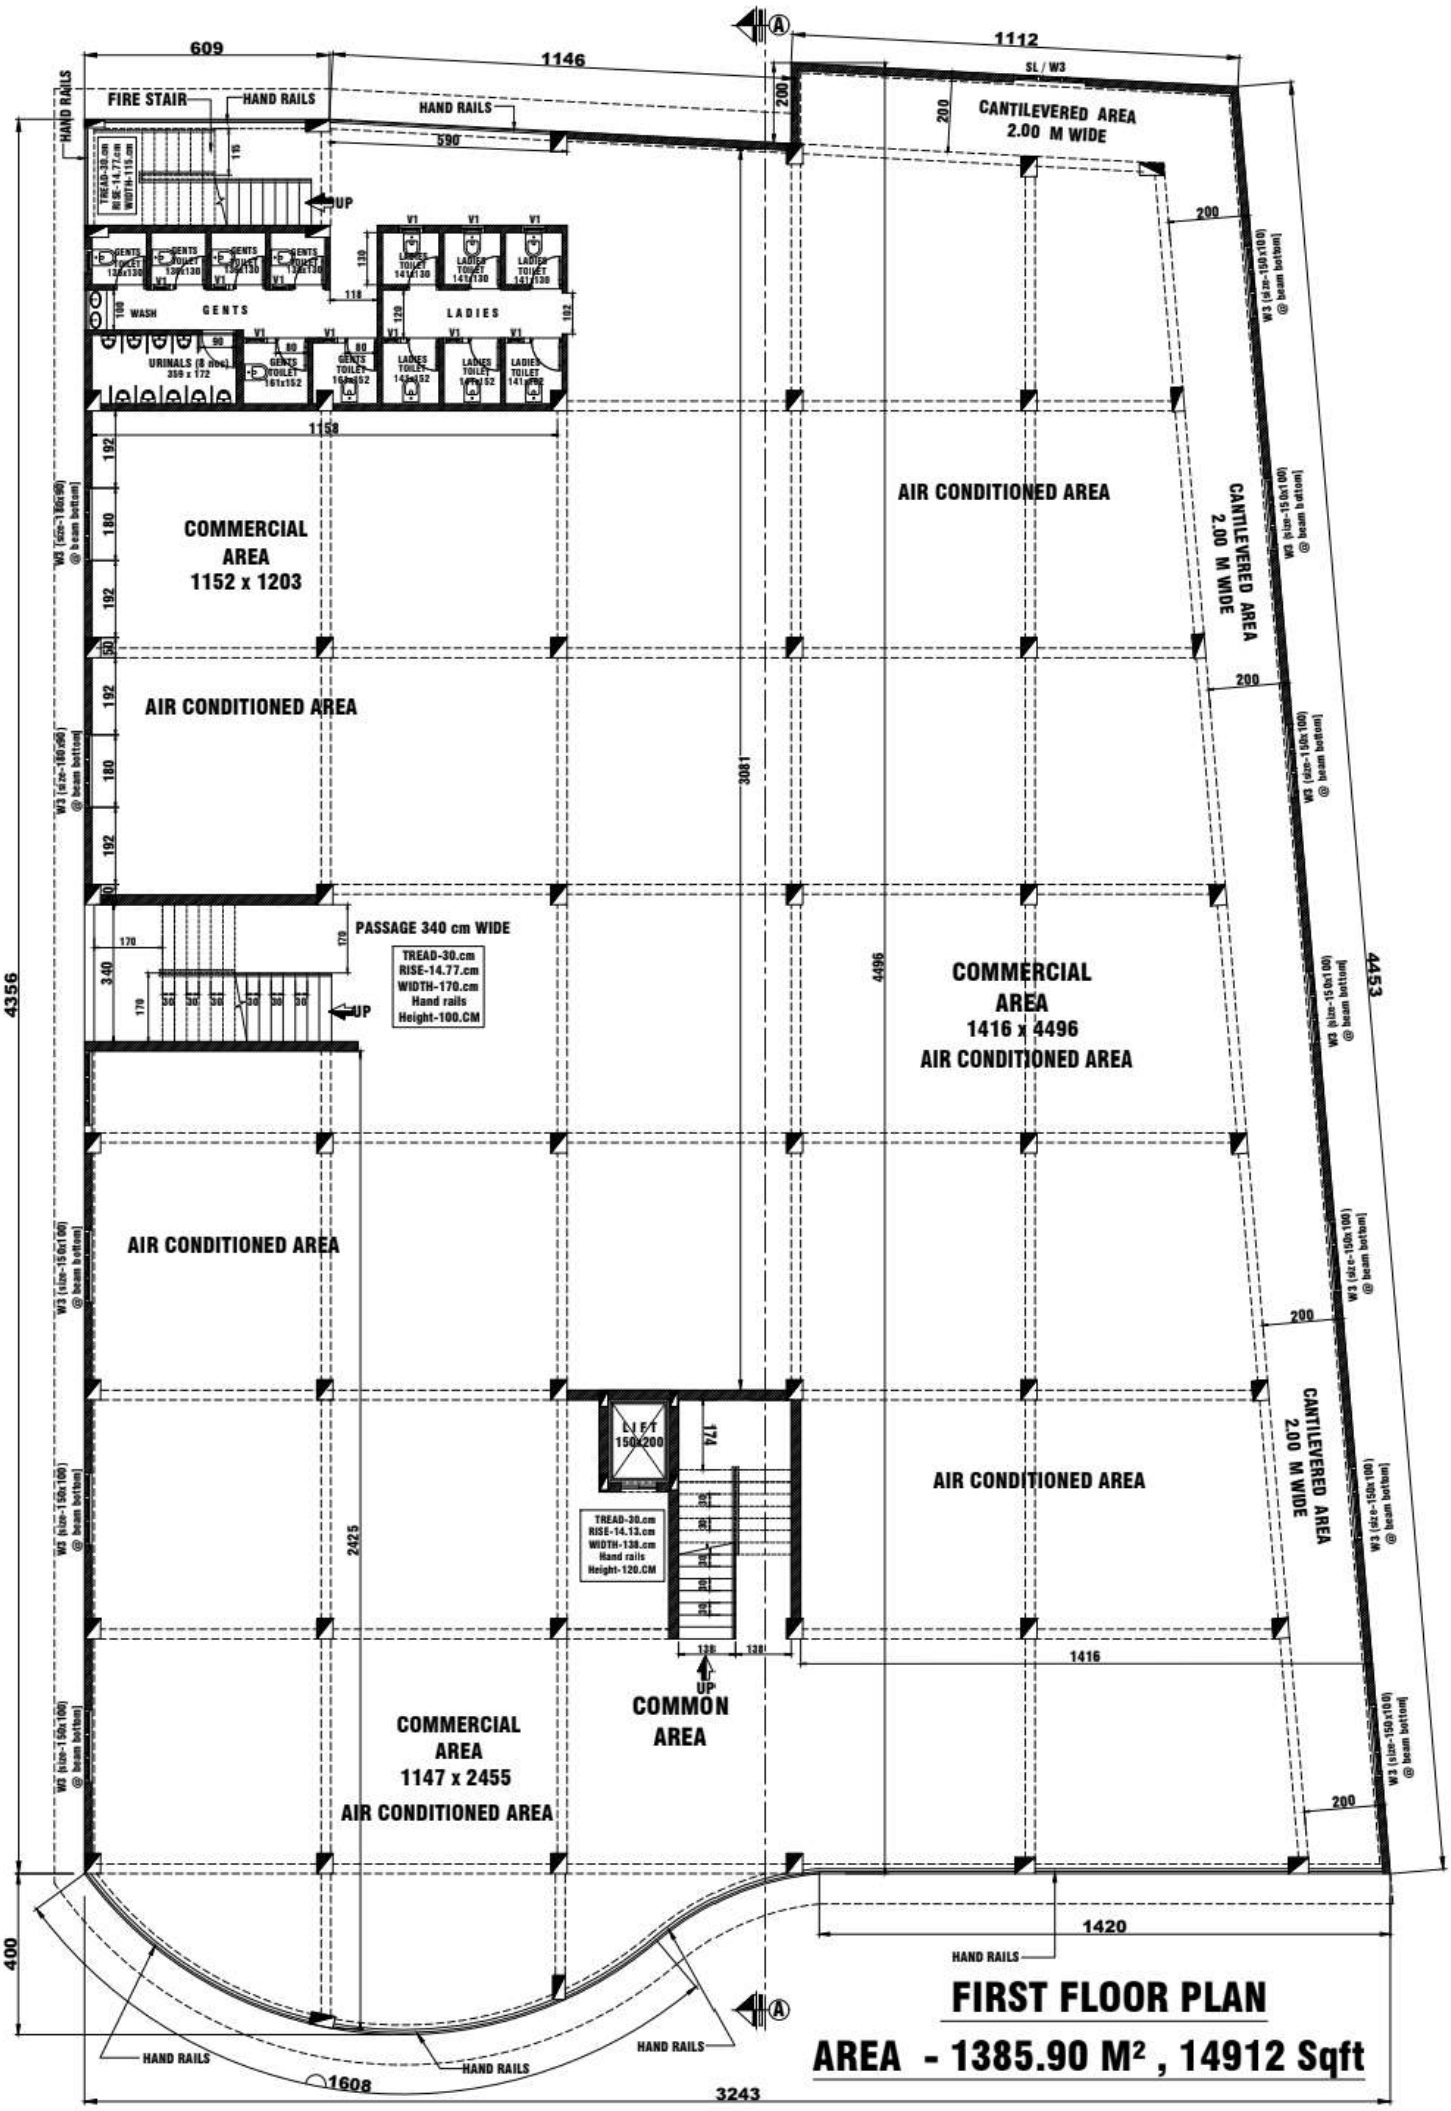
FIRST FLOOR PLAN
AREA - 1385.90 M², 14912 Sqft
FIRE STAIR
HAND RAILS
CANTILEVERED AREA 2.00 M WIDE
COMMERCIAL AREA 1152 x 1203
AIR CONDITIONED AREA
PASSAGE 340 cm WIDE
TREAD-30.cm RISE-14.77.cm WIDTH-170.cm Hand rails Height-100.CM
COMMERCIAL AREA 1416 x 4496 AIR CONDITIONED AREA
LIFT 150x200
TREAD-30.cm RISE-14.13.cm WIDTH-138.cm Hand rails Height-120.CM
COMMON AREA
COMMERCIAL AREA 1147 x 2455 AIR CONDITIONED AREA
GENTS
LADIES
WASH
URINALS (8 nos) 359 x 172
UP
4356
4453
3243
1608
1420
1416
4496
3081
2425
1146
1112
609
590
1158

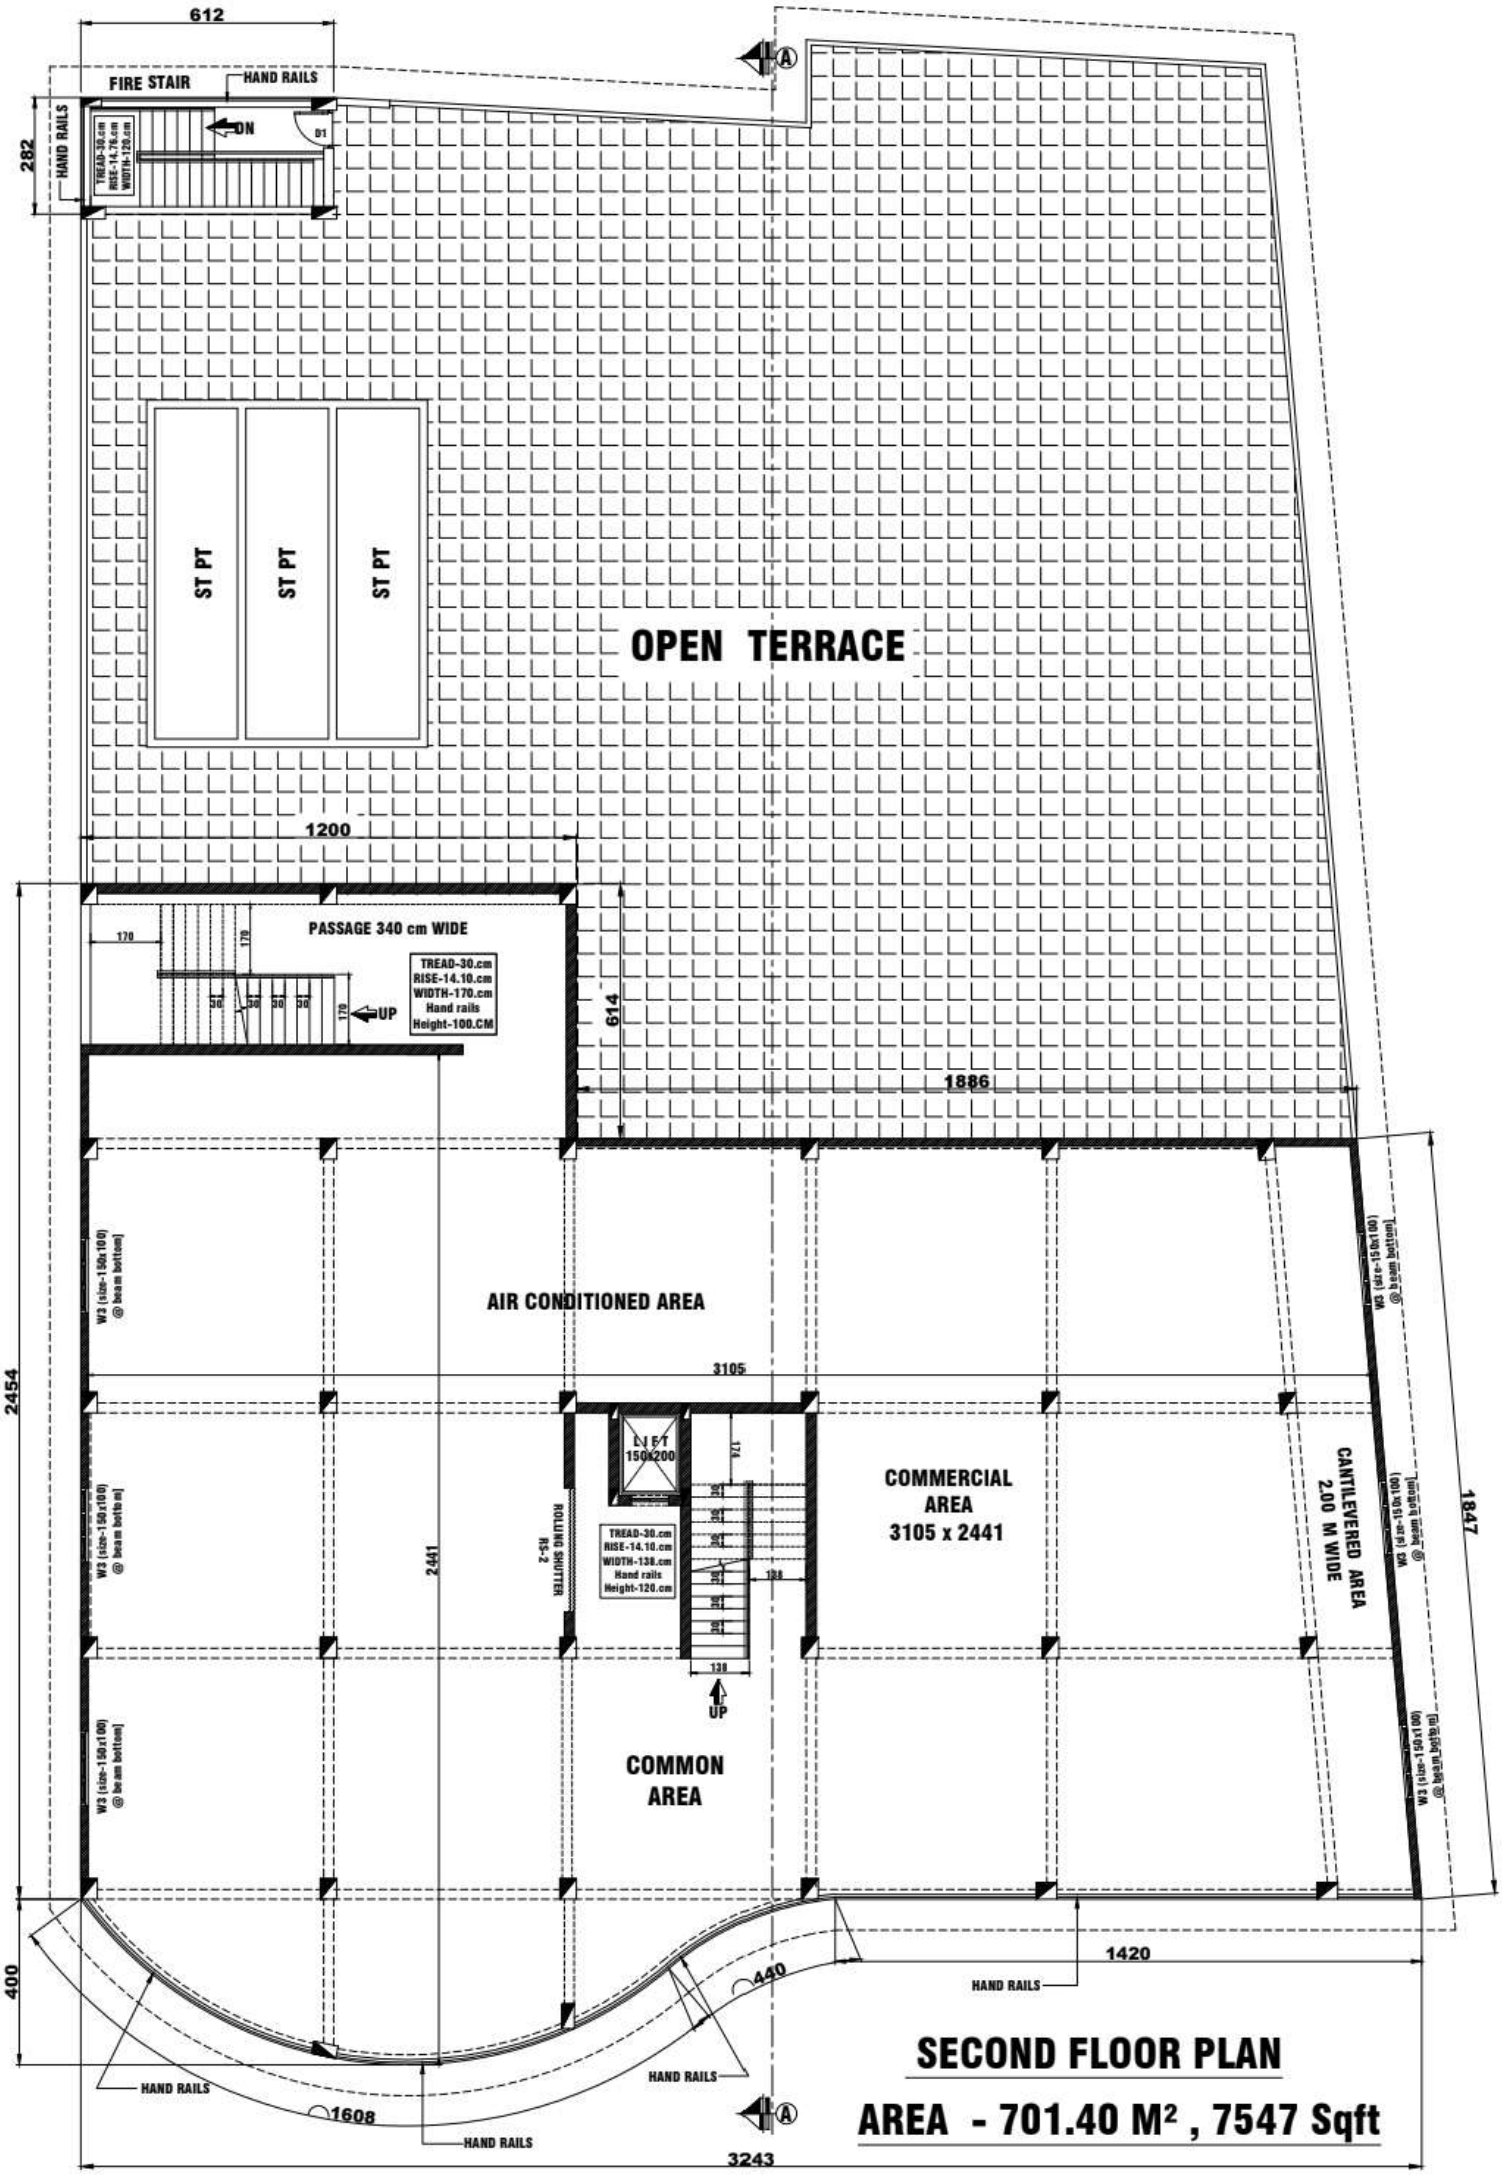

SECOND FLOOR PLAN

AREA - 701.40 M², 7547 Sqft

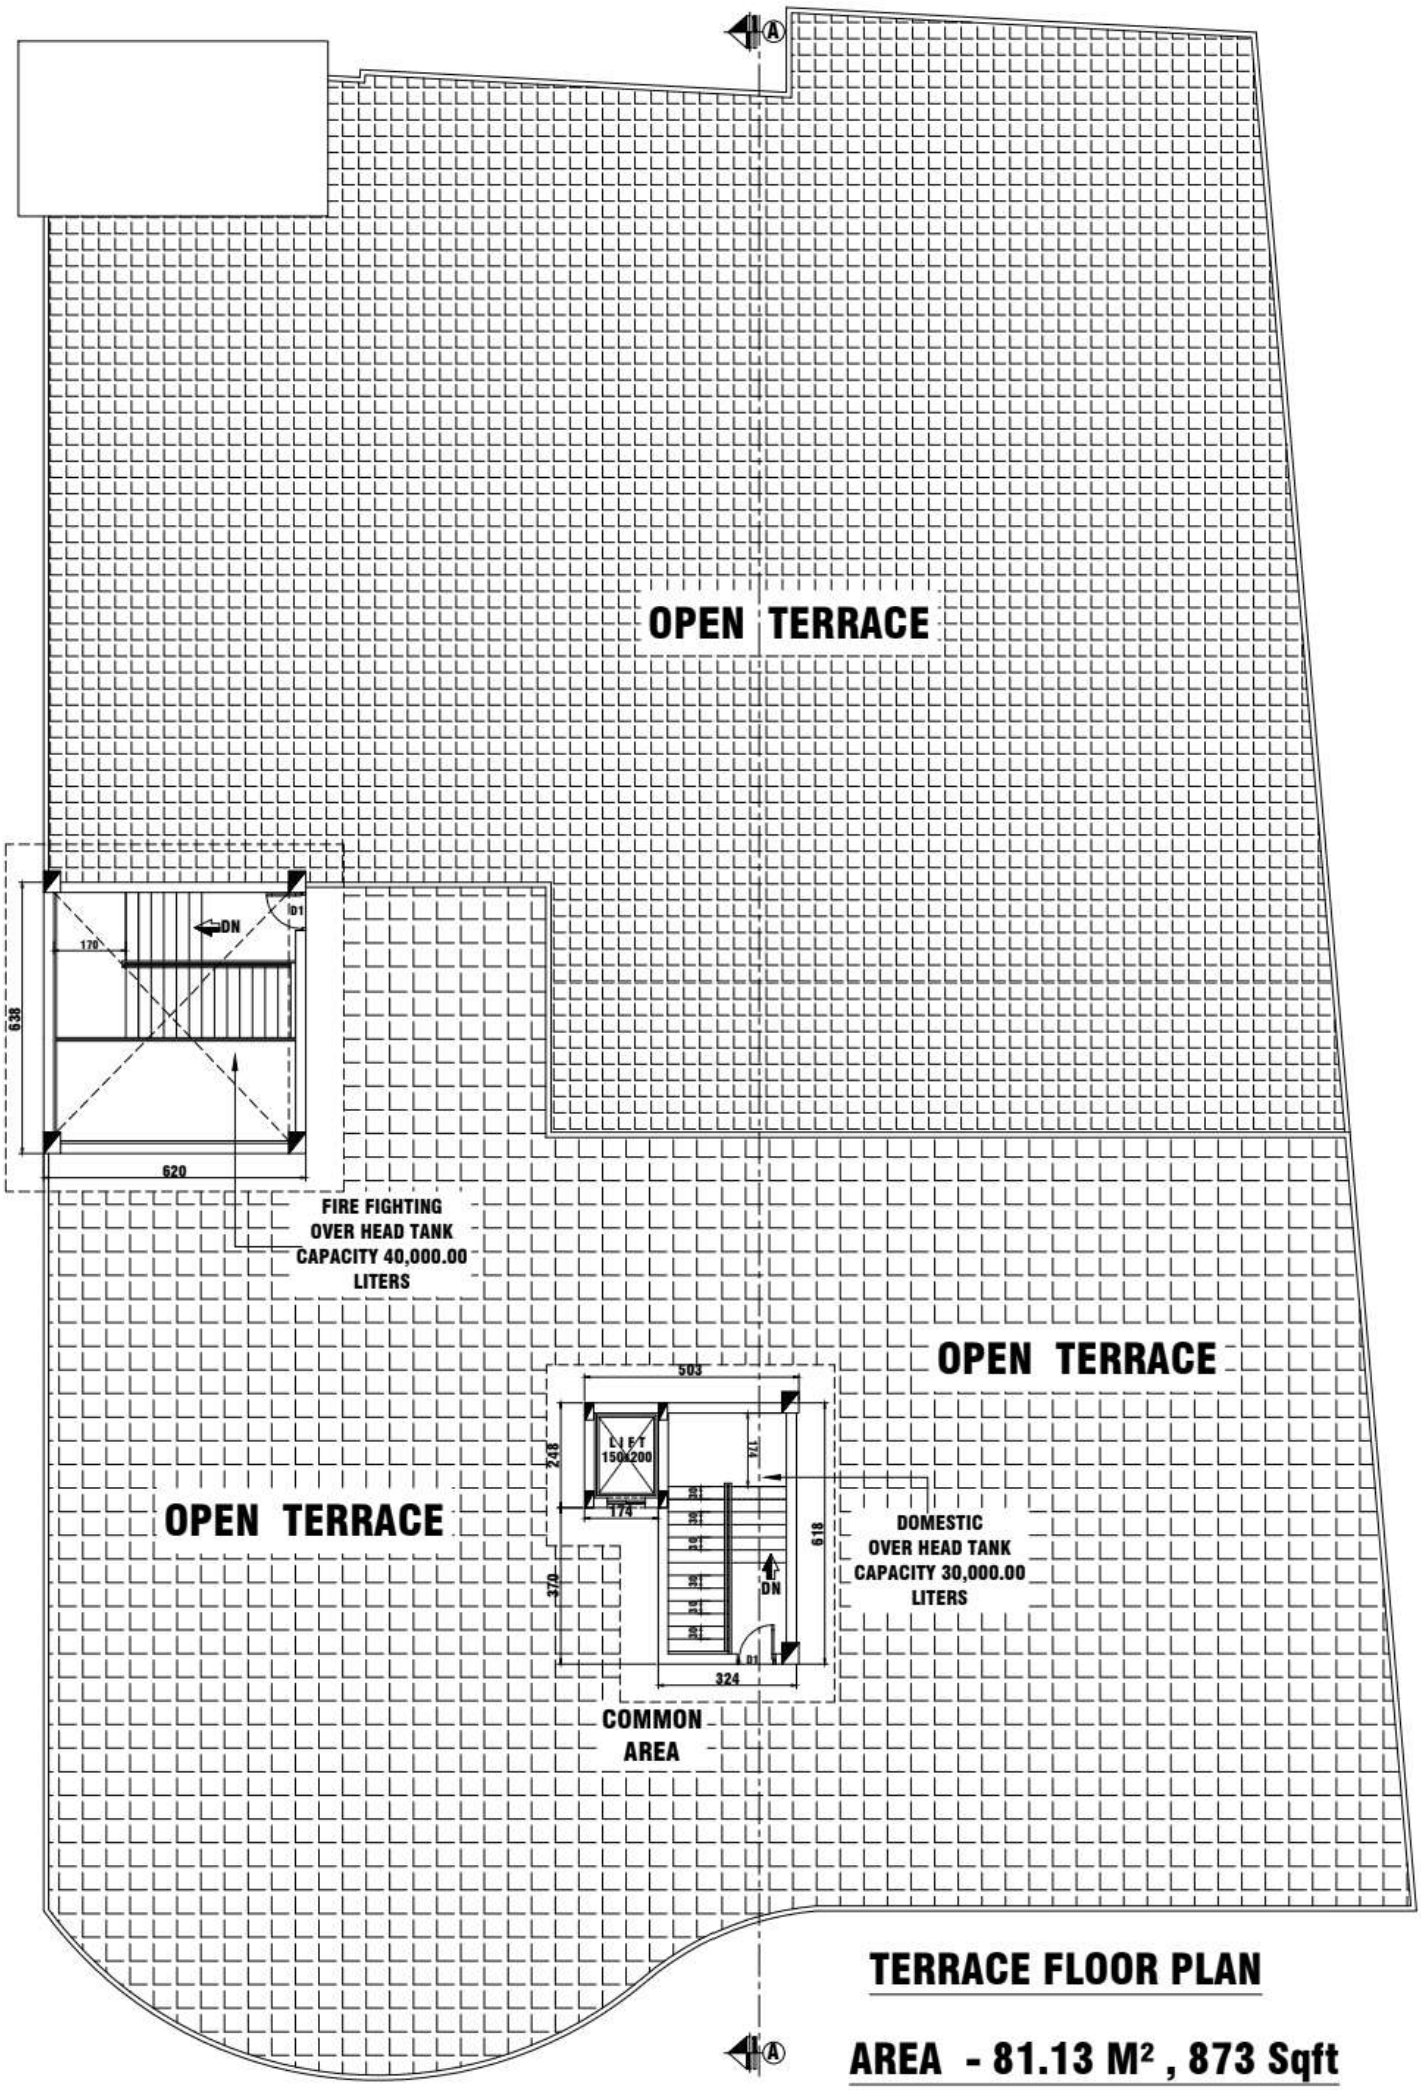

TERRACE FLOOR PLAN

AREA - 81.13 M², 873 Sqft